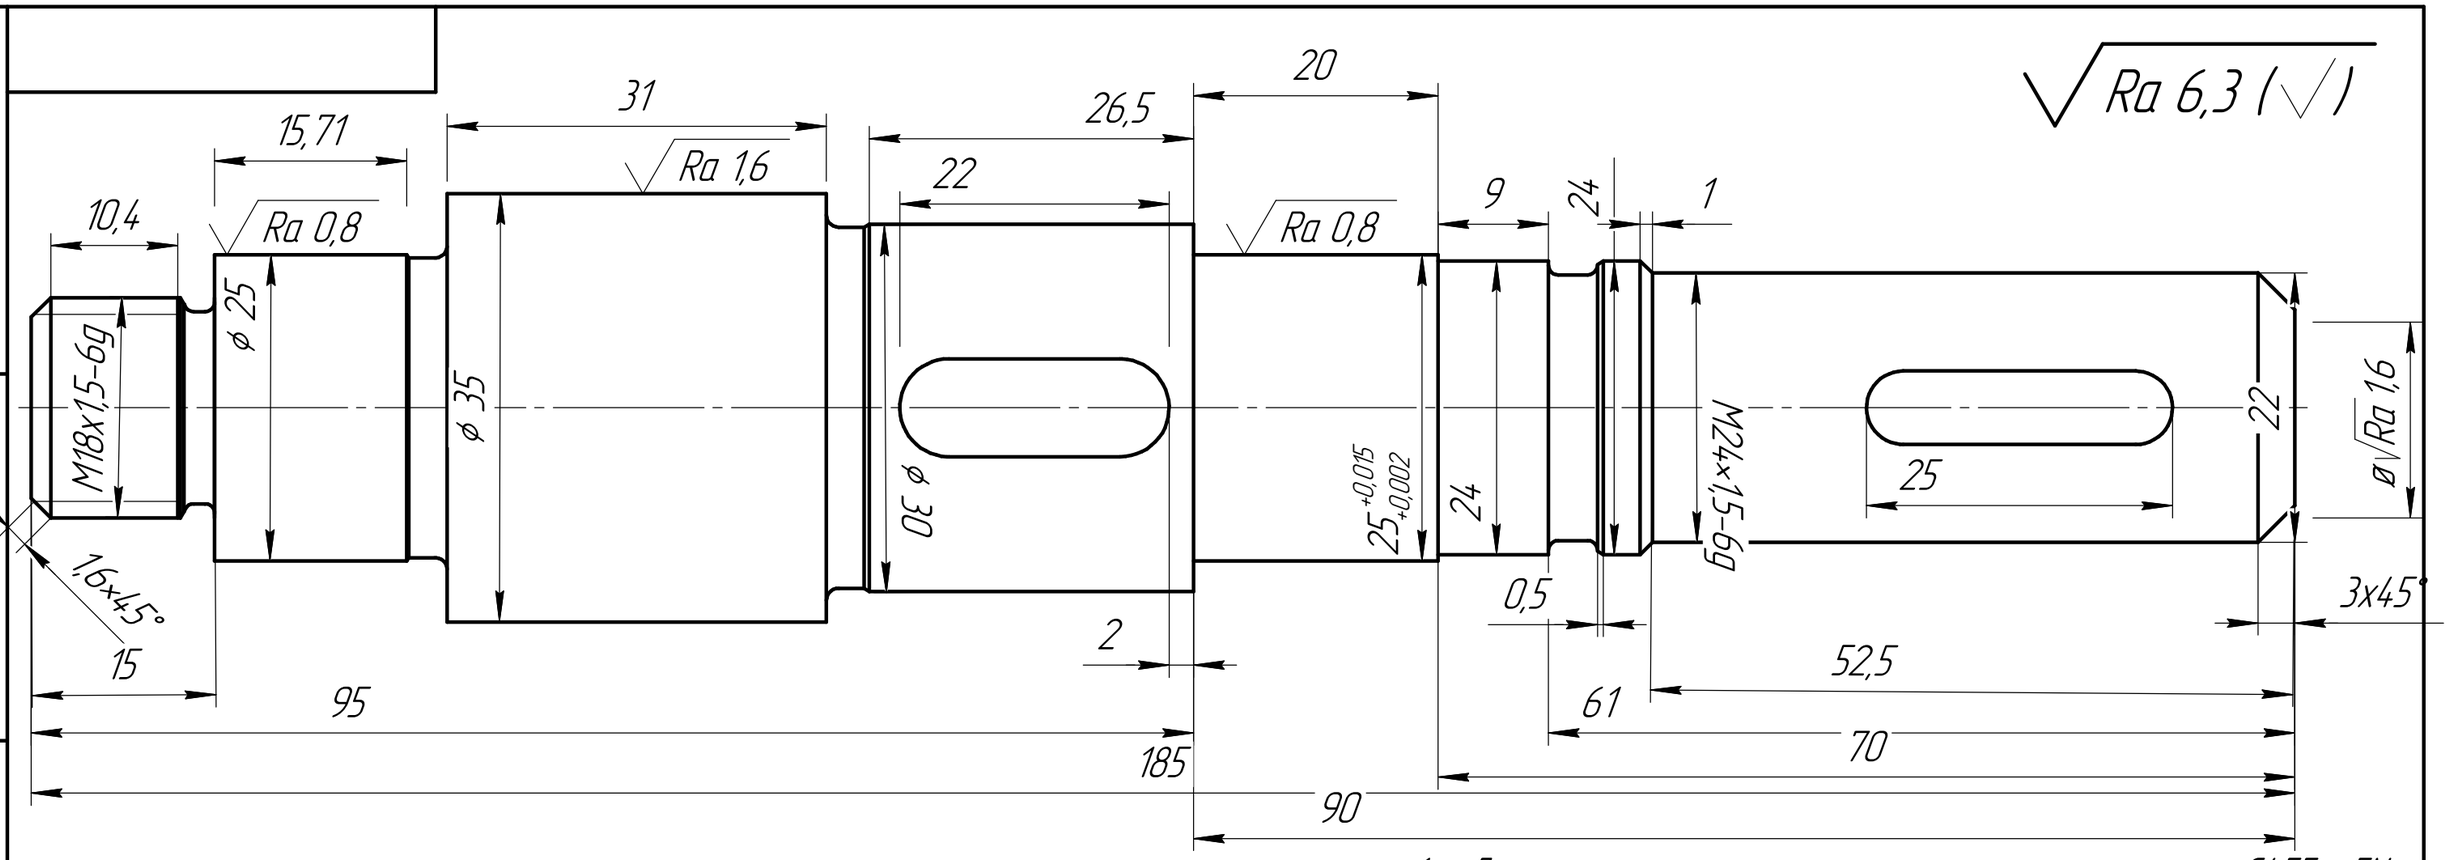


1. Допускается замена материала на сталь C45E EN 10083-2.

2. Твердость 45...50 HRC, кроме мест, указанных особо.

3. Неуказанные предельные отклонения размеров: валов h14, отверстий H14, остальных ±IT14/2.

4. Неуказанные радиусы галтелей 1,5 мм.

5. Формообразующие элементы, острые кромки и заусенцы притупить фасками 0,5x45° или радиусом 0,5 мм.

7. Биение опорных шеек относительно оси вала не более 0,02 мм.

8. Покрытие Хим. Окс. прм.

Изм.	Лист	№ докум.	Подп.	Дата			
Разраб.		Майорова Мила		13.10.2022	Вал ступенчатый	Лит.	Масса 0,78	Масштаб 1:1
Пров.						Лист	Листов 1	
Т. контр.								
Н. контр.					Сталь 45 ГОСТ 1050-2013			
Утв.								

Перв. примен.

Справ. №

Подп. и дата | Инв. № подл. | Подп. и дата | Взам. инв. № | Инв. № дубл. |

КОМПАС-3D v25 Учебная версия © 2026 ООО "АСКОН-Системы проектирования". Россия. Все права защищены

Не для коммерческого использования

Копировал

Формат А3